AIRCRAFT PARKING/DOCKING CHART - ICAO

TATRY VEŽA/TOWER **121,350** (118,950)


APRON ELEV 696 m

LZTT
POPRAD-Tatry

STAND	CRITICAL TYPE
1	B738W
2	DH8D
3	B738W
4	B738W

NOTE: DUE TO WIND DIRECTION OR OPERATIONAL REASONS ACFT PARKING ON APN OUT OF REGULAR STANDS POSITIONS POSSIBLE BY ASSISTANCE OF TWR INSTRUCTIONS OR APN MARSHALLER SIGNALS.

INS COORDINATES FOR AIRCRAFT STANDS			
1	49°04'10,43"N	020°14'53,37"E	ACL = 696 m
2	49°04'08,98"N	020°14'51,73"E	ACL = 696 m
3	49°04'07,94"N	020°14'49,27"E	ACL = 696 m
4	49°04'08,57"N	020°14'46,40"E	ACL = 696 m

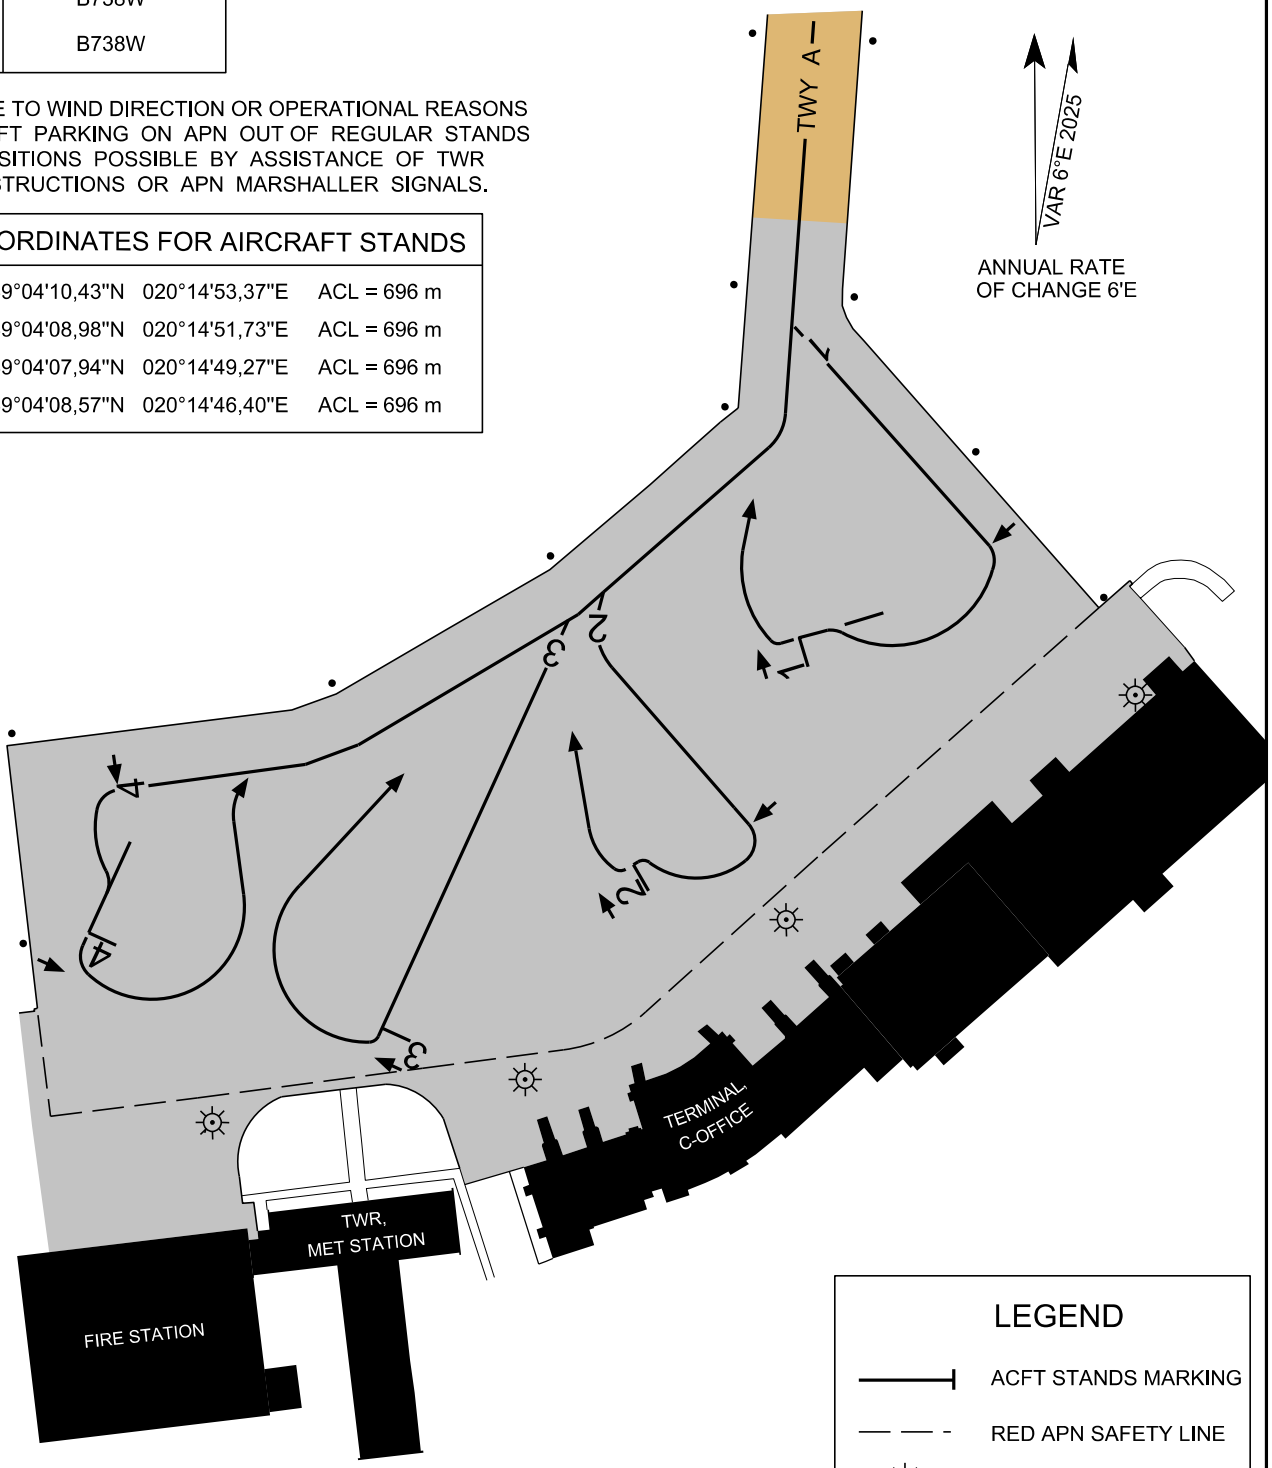

TAXIWAY	WIDTH	SURFACE	STRENGTH
A	19 m	asphalt	PCN 40/F/A/X/T

APRON	asphalt	PCN 40/F/A/X/T

SCALE 1 : 1 500

LEGEND

- ACFT STANDS MARKING
- RED APN SAFETY LINE
- LIGHTING MASK
- TAXIWAY LIGHTS
- DAY MARKING BY YELLOW COLOUR

CHANGES: MAG VAR

METRES 50 0 50

FEET 100 0 100 200