
AERODROME CHART - ICAO

ARP = 49°04'25"N 020°14'28"E
AD ELEV 718 m

TATRY VEŽA/TOWER **121,350** (118,950)

POPRAD-Tatry

ELEVATIONS AND DIMENSIONS ARE IN METRES

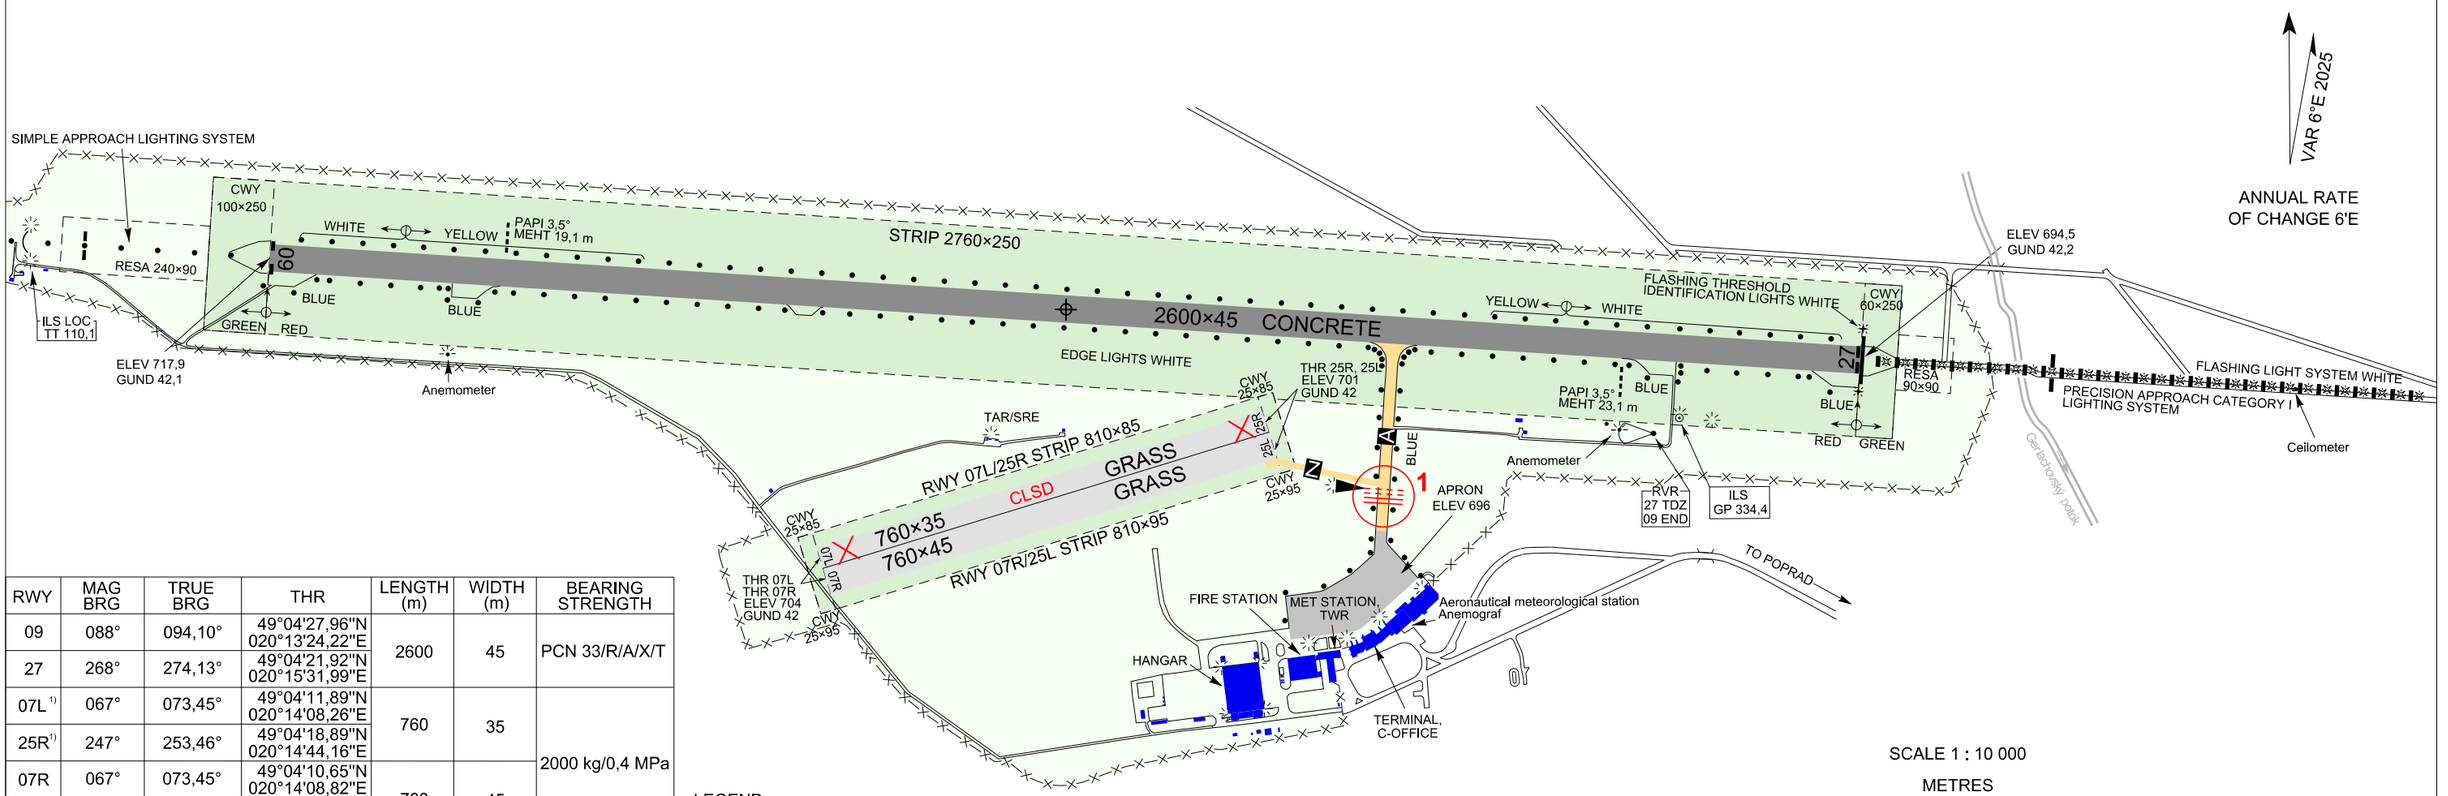

RWY	MAG BRG	TRUE BRG	THR	LENGTH (m)	WIDTH (m)	BEARING STRENGTH
09	088°	094,10°	49°04'27,96"N 020°13'24,22"E	2600	45	PCN 33/R/A/X/T
27	268°	274,13°	49°04'21,92"N 020°15'31,99"E			
07L [1]	067°	073,45°	49°04'11,89"N 020°14'08,26"E	760	35	2000 kg/0,4 MPa
25R [1]	247°	253,46°	49°04'18,89"N 020°14'44,16"E			
07R	067°	073,45°	49°04'10,65"N 020°14'08,82"E	760	45	
25L	247°	253,46°	49°04'17,65"N 020°14'44,72"E			
TAXIWAY [2]			TWY A		19	PCN 40/F/A/X/T
			TWY Z		10	2000 kg/0,4 MPa

[1] RWY closed
[2] see LZTT AD 2.20.6 Taxiing - limitations

LEGEND

RWY (area of ATC responsibility)
TWY (area of ATC responsibility)
APN
RWY strip
AD area


HOT SPOT:

1	The possibility of overlooking the holding point's marking on TWY A before the entrance on RWY 09/27. No crossing any one of RWY's and TWY A without permission of TWR (121,350 MHz).

SCALE 1 : 10 000

METRES
400 300 200 100 0 500 1000
1000 500 0 1000 2000 3000
FEET

MARKINGS ON MANOEUVRING AREA

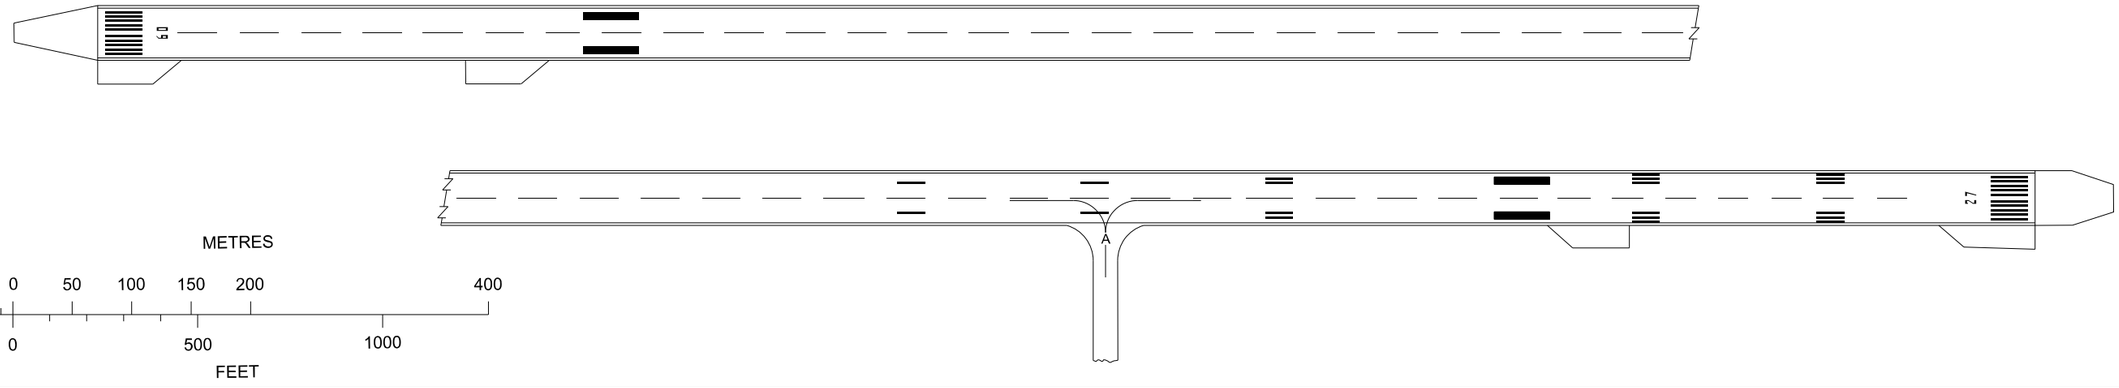

CHANGES: RWY MAG BRG; MAG VAR